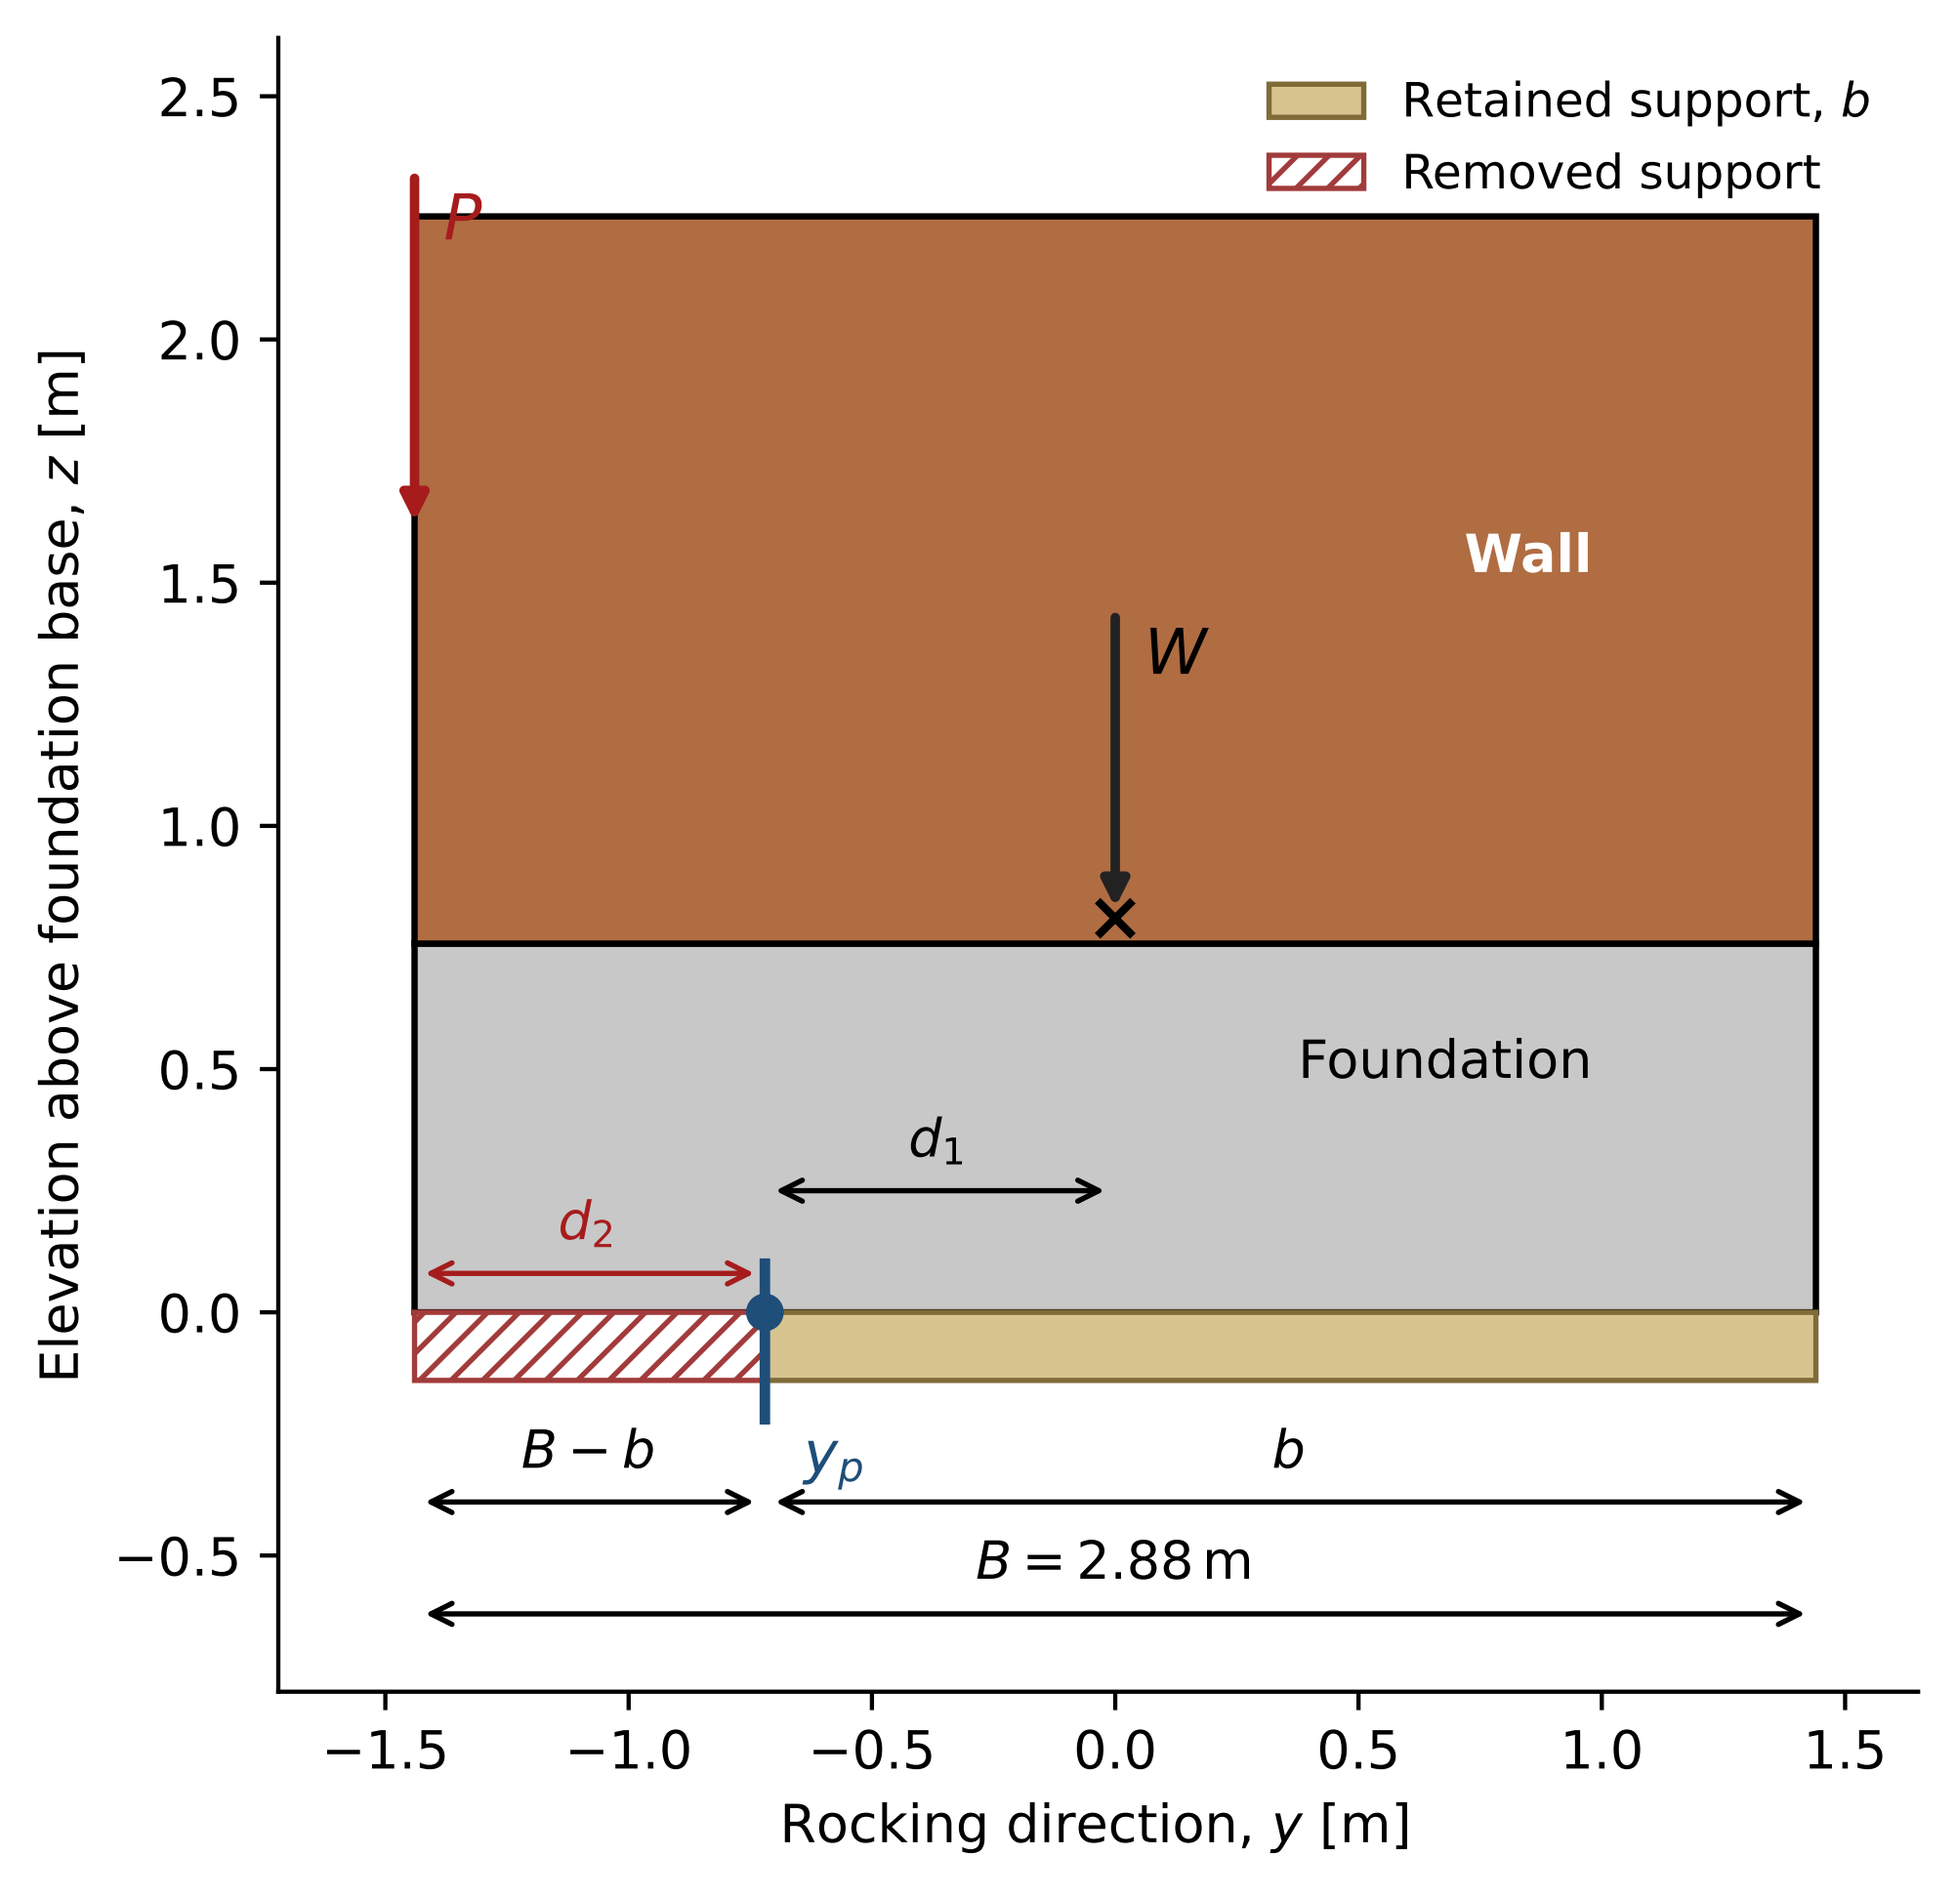
Retained support, b
Removed support
P
Wall
W
Foundation
d_1
d_2
$B - b$
y_p
b
$B = 2.88\,\mathrm{m}$
Elevation above foundation base, z [m]
Rocking direction, y [m]
2.5
2.0
1.5
1.0
0.5
0.0
−0.5
−1.5
−1.0
−0.5
0.0
0.5
1.0
1.5